



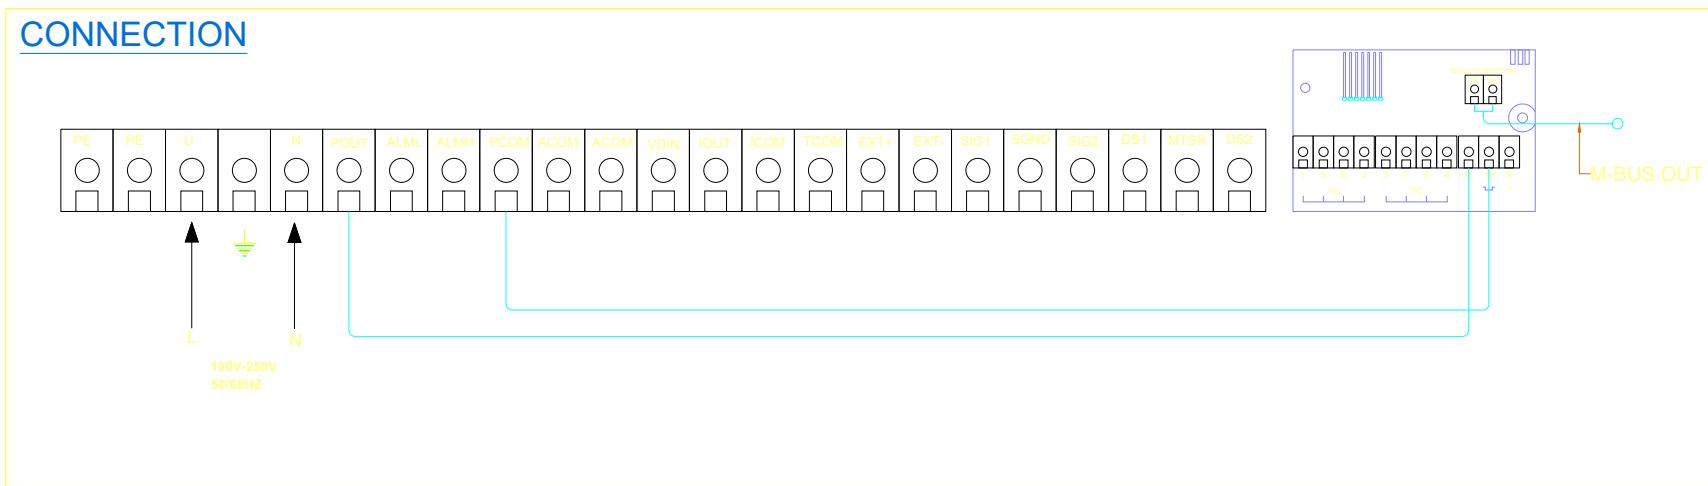

SIZE	Nominal Pressure	L	ØD	ØA	H	N-Øh
450	PN16	600	565	515	658	16-Ø26
600		600	780	725	882	20-Ø30

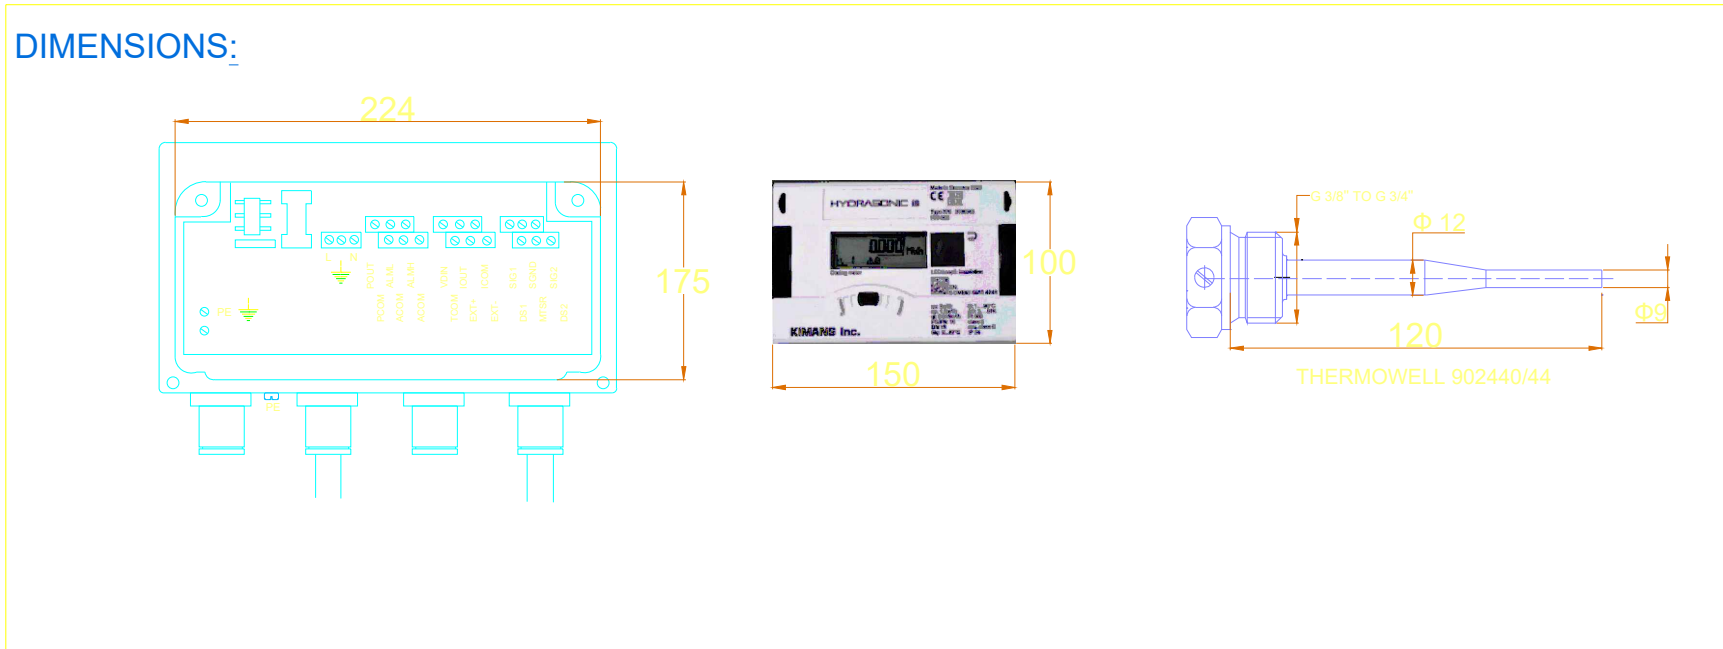

SG1	SIGNAL 1	REMOTE SENSOR
SGND	SIGNAL GROUND	
SG2	SIGNAL 2	
DS1	SHIELDED EXTING 1	ANALOG CURRENT OUTPUT
DS2	SHIELDED EXTING 2	
EXT1	EXTING CURRENT +	
EXT-	EXTING CURRENT -	FREQUENCY (PULSE) OUTPUT
VSIN	CURRENT TWO LINES 24V SPOTS	
IOUT	ANALOG CURRENT OUTPUT	
IDOM	ANALOG CURRENT OUTPUT GROUND	TOW ALARM OUTPUTS
POUT	LOW FREQUENCY (PULSE) OUTPUT	
PCOM	FREQUENCY (PULSE) OUTPUT GROUND	
ALM1	UPPER LIMIT ALARM OUTPUT	COMMUNICATION
ALM2	LOW LIMIT ALARM OUTPUT	
ALCOM	ALARM OUTPUT GROUND	
TSIN	COMMUNICATION INPUT (RS485-A)	COMMUNICATION
TRM	COMMUNICATION INPUT (RS485-B)	
TCOM	COMMUNICATION GROUND	

ELECTROMAGNETIC FLOWMETER

